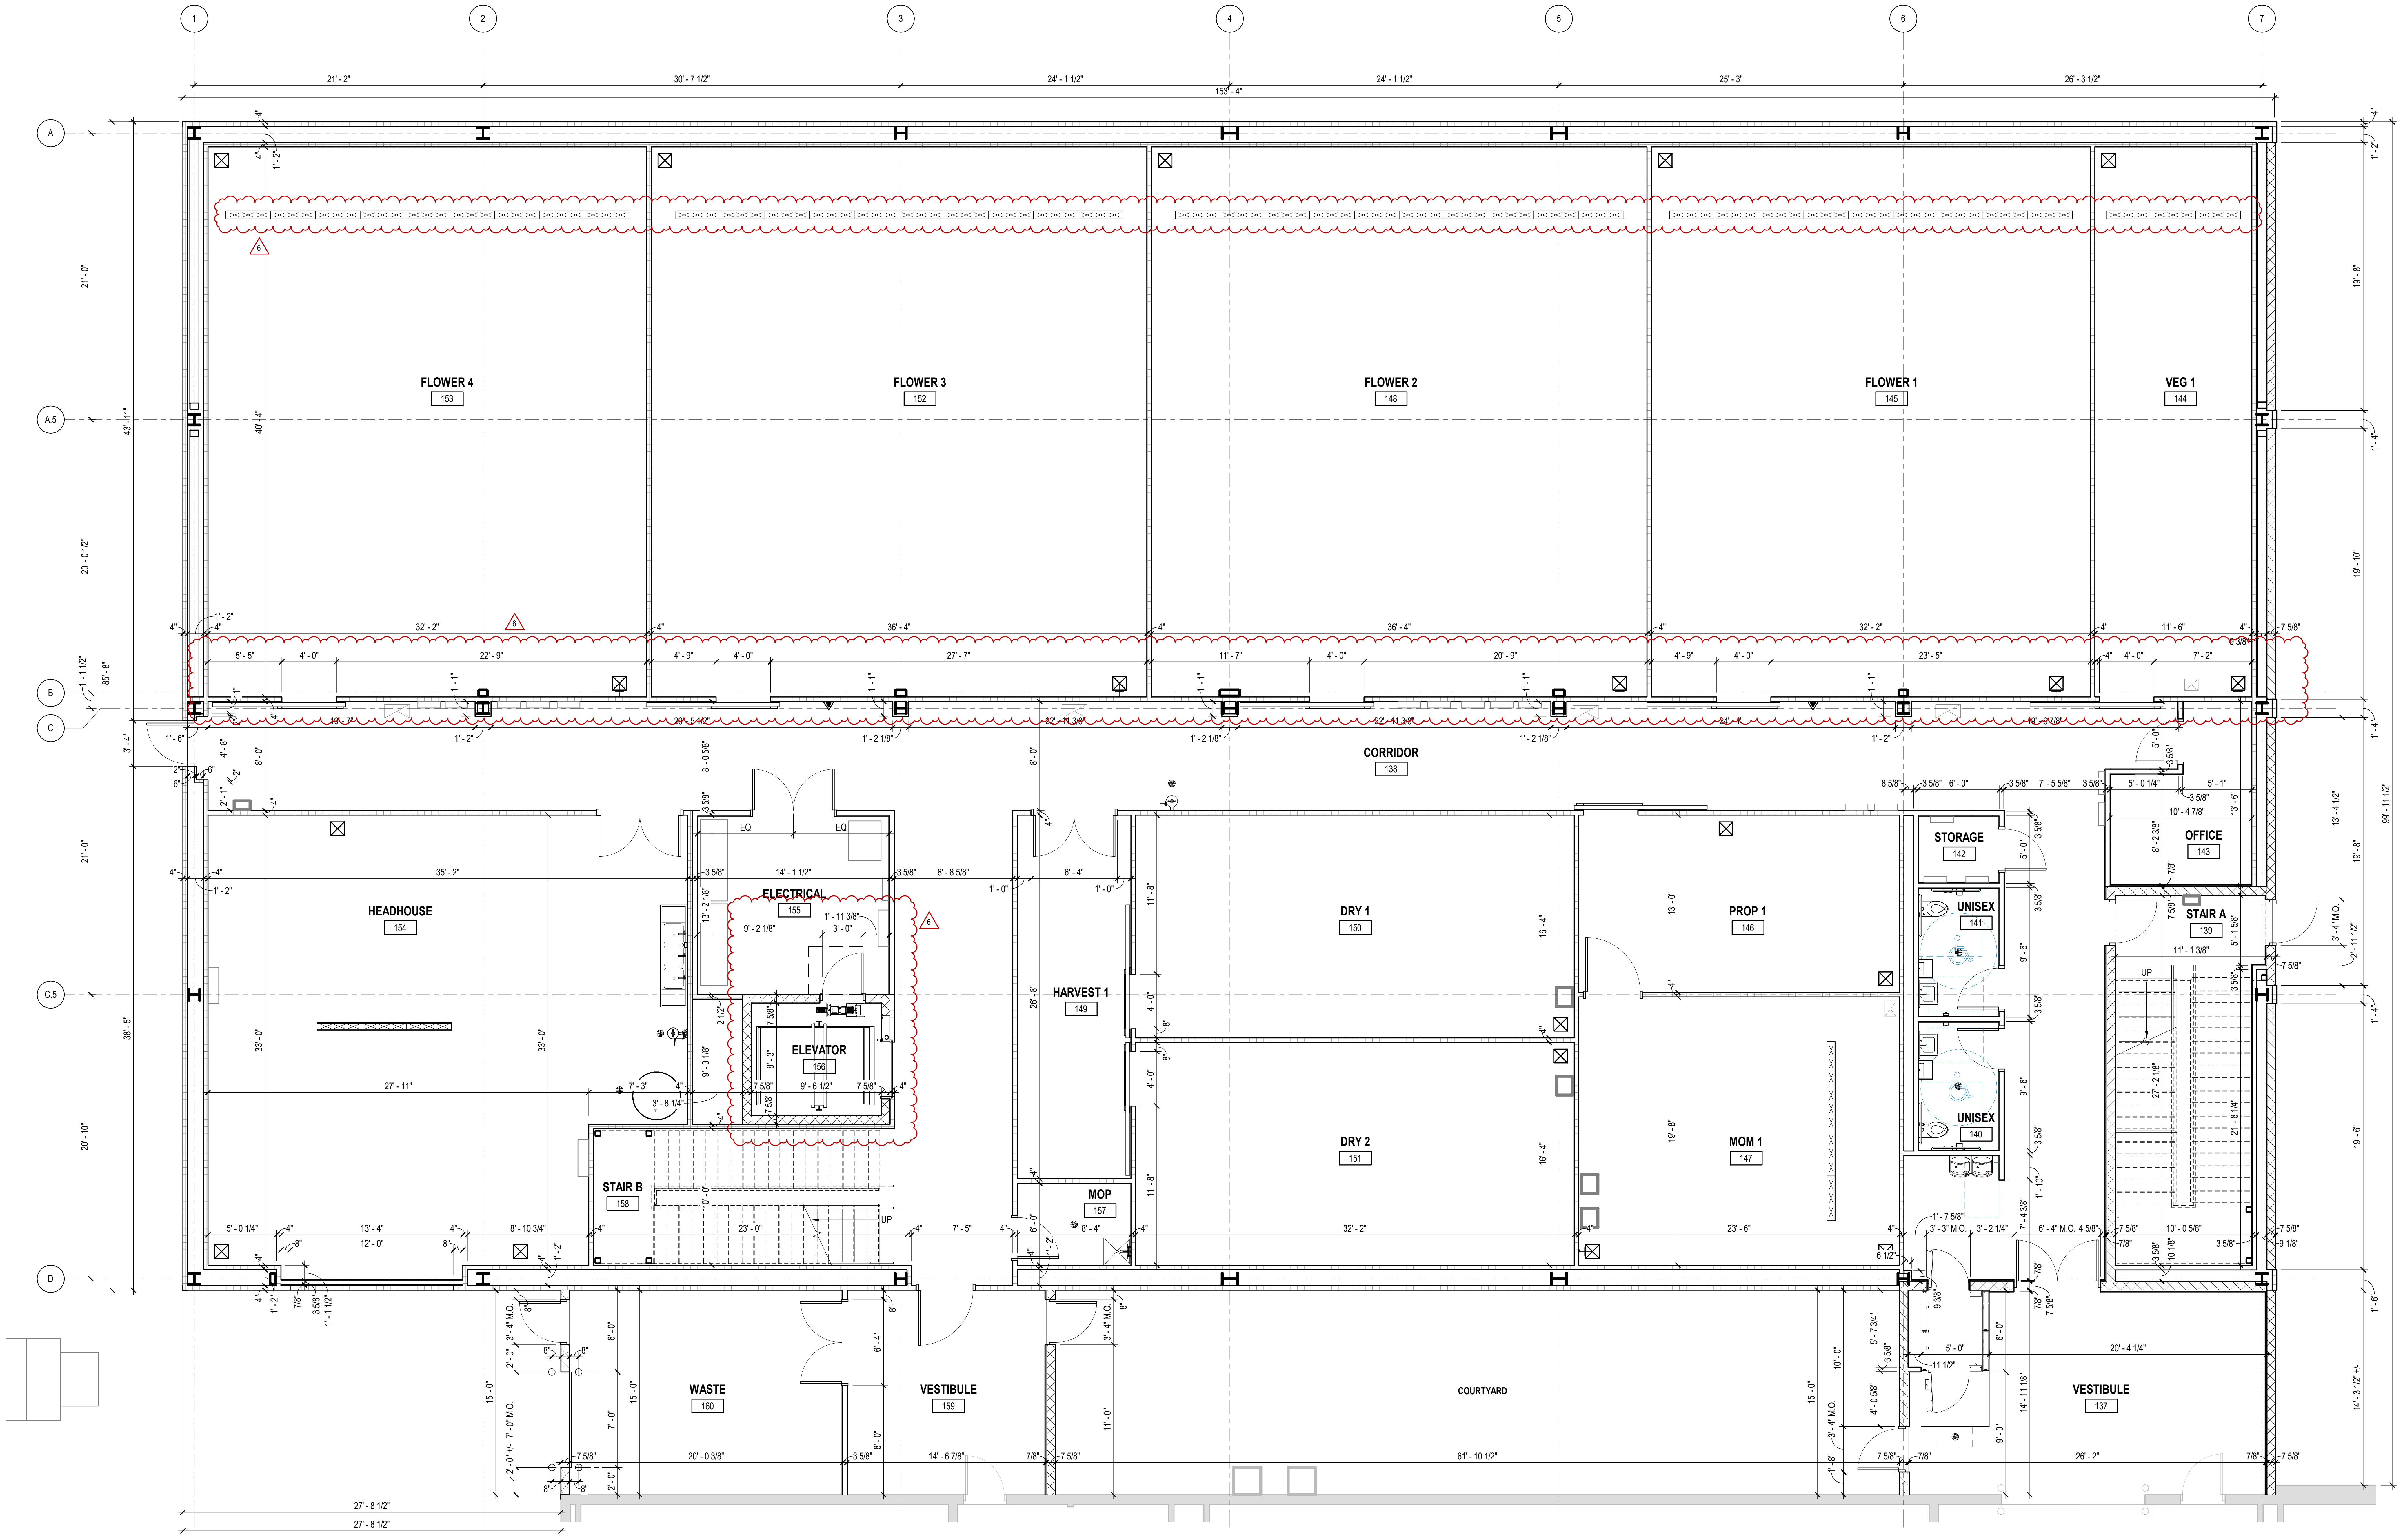
1
2
3
4
5
6
7
A
A.5
B
C
C.5
D
21' - 2"
30' - 7 1/2"
24' - 1 1/2"
24' - 1 1/2"
25' - 3"
26' - 3 1/2"
153' - 4"
FLOWER 4
153
FLOWER 3
152
FLOWER 2
148
FLOWER 1
145
VEG 1
144
CORRIDOR
138
HEADHOUSE
154
ELECTRICAL
155
ELEVATOR
156
STAIR B
158
HARVEST 1
149
MOP
157
DRY 1
150
DRY 2
151
PROP 1
146
MOM 1
147
STORAGE
142
UNISEX
141
UNISEX
140
OFFICE
143
STAIR A
139
WASTE
160
VESTIBULE
159
COURTYARD
VESTIBULE
137
27' - 8 1/2"
61' - 10 1/2"
UP


AREA OF ADDITION
AREA OF ALTERATION

FIRST FLOOR KEYPLAN

NOT TO SCALE

CORE DESIGN GROUP

155 WEST MARKET STREET, SUITE 200
YORK, PA 17401

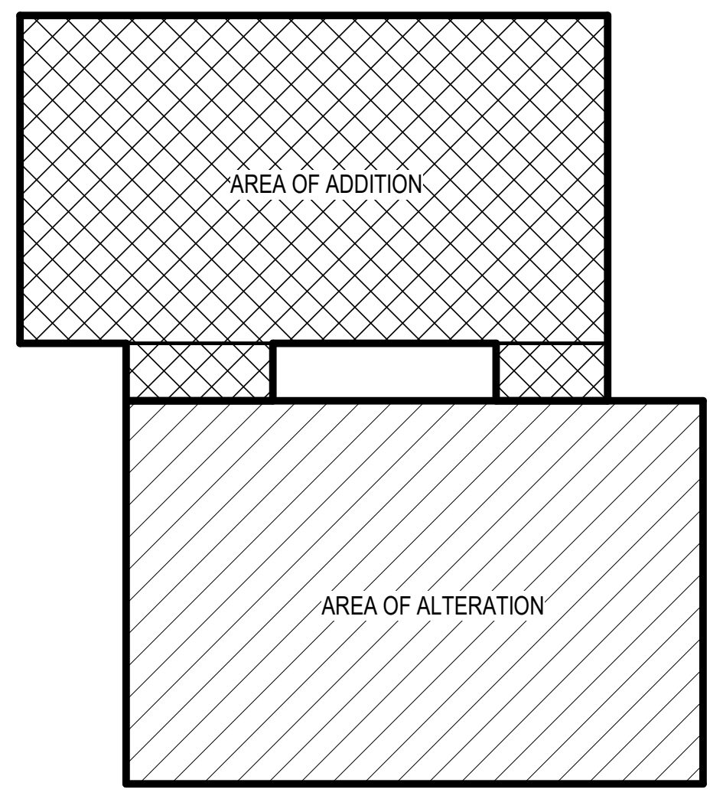WWW.CORE-DESIGNGROUP.COM

PHONE 717.741.2046 FAX: 717.741.6836

SEAL/STAMP:

ASCENSION BIOMEDICAL ADDITION & RENOVATION

200 ARTINO STREET
OBERLIN, OH
CITY OF OBERLIN / LORAIN COUNTY

THE GROW FACILITY COMPANY
DAG
CONTROLLED ENVIRONMENT AGRICULTURE

DAG
RECEIVED
October 16, 2024

ALL PARTS OF THESE DOCUMENTS AND/OR SPECIFICATIONS ARE THE EXCLUSIVE PROPERTY OF THE ARCHITECT AND WE RESERVE ALL RIGHTS TO HAVE THIS WORK REPRODUCED, FABRICATED, CONSTRUCTED, AND/OR MANUFACTURED. WE HAVE PLACED THESE DOCUMENTS IN YOUR TEMPORARY CUSTODY, IN CONFIDENCE, SOLELY FOR YOUR INSPECTION, AND/OR ESTIMATING THE COST OF FABRICATING, CONSTRUCTING, AND/OR MANUFACTURING THE WORK SHOWN. THE CONTRACTOR IS RESPONSIBLE FOR CHECKING ALL DIMENSIONS AND CONDITIONS AT THE JOBSITE, AS WELL AS BUILDING RULES AND REGULATIONS. THE CONTRACTOR IS RESPONSIBLE FOR COORDINATING ALL INSPECTIONS AND OBTAINING THE CERTIFICATE OF OCCUPANCY. THE RECIPIENT OF THESE DOCUMENTS WARRANTS THAT THEY WILL NOT REPRODUCE, DISTRIBUTE, OR OTHERWISE MAKE USE OF THE DOCUMENTS WITHOUT THE PERMISSION OF THE ARCHITECT. THE USE OF THESE DESIGNS FOR ANY OTHER PURPOSE IS UNAUTHORIZED. DO NOT SCALE THESE DOCUMENTS.

REVISIONS

NO.	DATE	DESCRIPTION
1	04.10.2024	ISSUED FOR PERMIT
2	05.08.2024	REVISION 1
	07.31.2024	CONFORMED SET
6	10.16.2024	REVISION 5

CURRENT
REVISION #5 2024.10.16

PROJECT NO:	PROJECT MGR:
2023.0270.00	K.L.C.

SHEET NAME:

FIRST FLOOR DIMENSION PLAN - AREA OF ADDITION

SHEET NO:

A111B

2024-10-16 11:45:47 AM Autodesk Docs://Ascension Biomedical - Oberlin, OH/2023.0270.00 Ascension Biomedical.rvt